
NOTE: REFER TO SHEETS C8.1 & A.2 FOR GENERAL FRAMING NOTES. SEE SHEET A.2 FOR WINDOW REQUIREMENTS AND STAIR CALCULATIONS AND REQUIREMENTS.

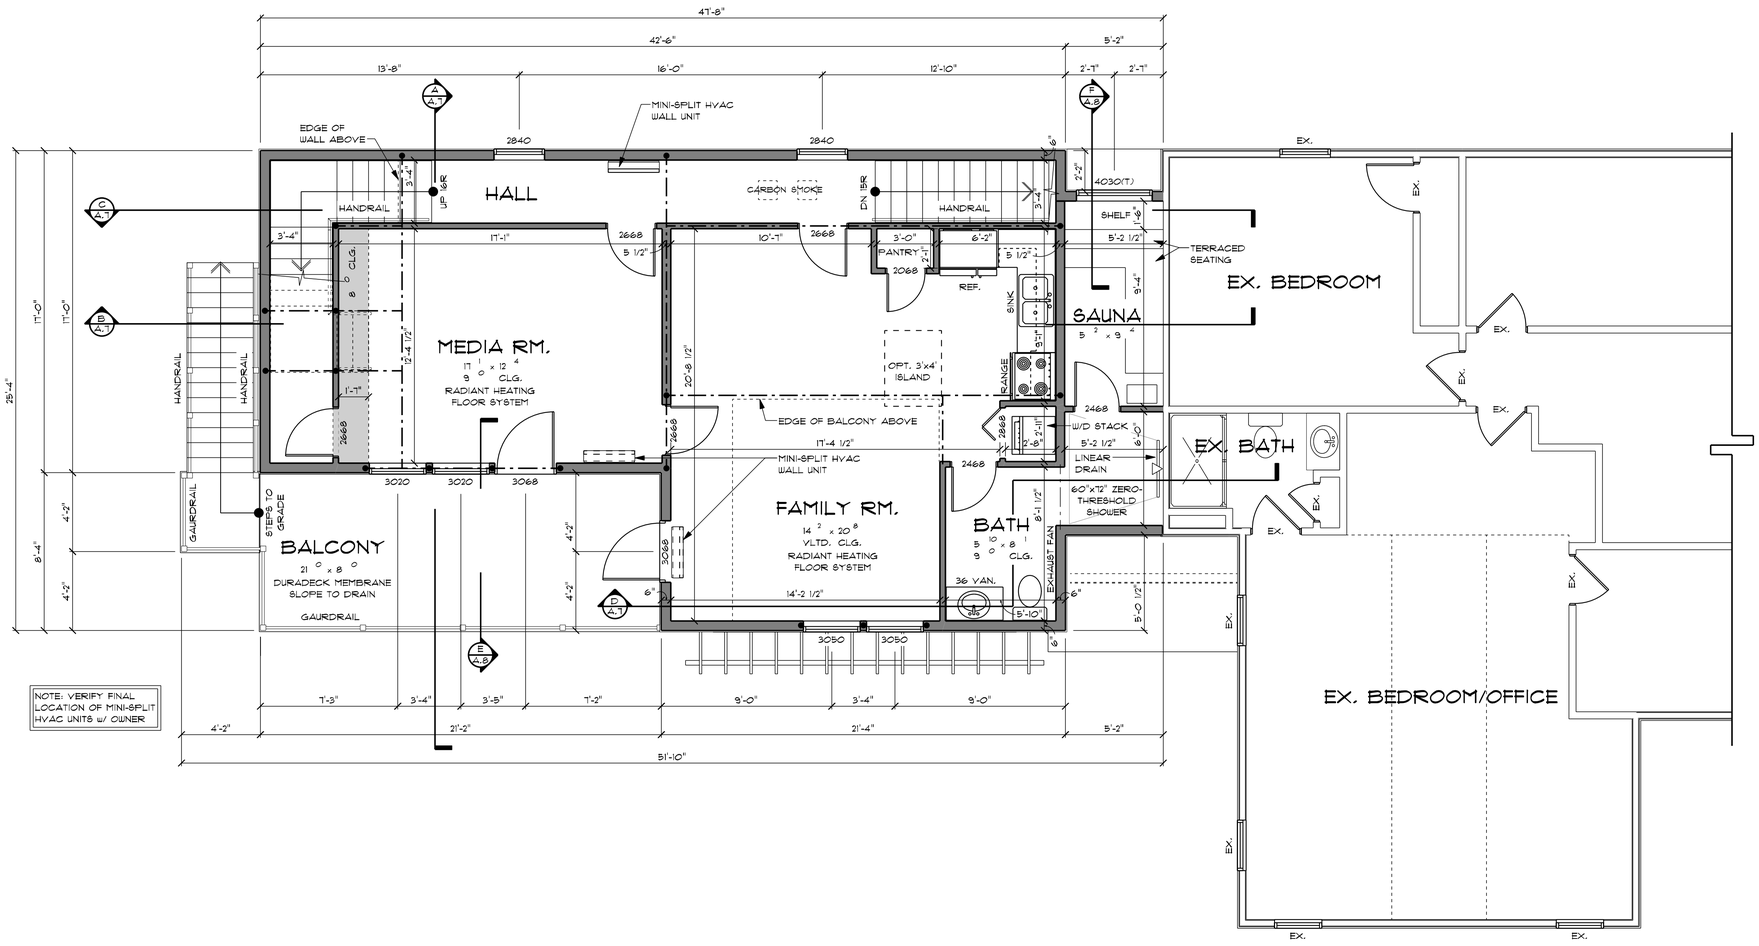

NOTE: VERIFY FINAL LOCATION OF MINI-SPLIT HVAC UNITS w/ OWNER

SECOND FLOOR PLAN
SCALE: 1/4" = 1'-0"

RESIDENTIAL Designed SOLUTIONS
Inspired Ideas. Proven Plans.

7844 FLINT ROAD
COLUMBUS, OHIO 43235
614 430-0027
FAX 430-8071

www.rdshomedesign.com

MEMBER BIA THE Builders Remodelers Council
MEMBER AIBD
NARI MEMBER
N·C·I·D·C

DATE	BY	REVISION

ANY DISCREPANCIES, ERRORS AND/OR OMISSION IN THE NOTES, DIMENSIONS AND OR DRAWINGS CONTAINED ON THESE DOCUMENTS SHALL BE BROUGHT TO THE ATTENTION OF THE DESIGNER PRIOR TO THE COMMENCEMENT OF CONSTRUCTION. PROCEEDING WITH CONSTRUCTION CONSTITUTES THE ACCEPTANCE OF THESE DOCUMENTS AND DISCREPANCIES, ERRORS AND/OR OMISSIONS BECOME THE RESPONSIBILITY OF THE BUILDING CONTRACTOR.

E.LAINE
(23027)

LAINE RESIDENCE
7111 PETER HOOVER RD.
NEW ALBANY (FRANKLIN), OHIO 43054

SECOND FLOOR PLAN

COPYRIGHT 2023
THE ARCHITECTURAL WORKS DEPICTED HEREIN ARE THE SOLE PROPERTY OF RESIDENTIAL DESIGNED SOLUTIONS, INC. AND MAY NOT BE CONSTRUCTED OR USED WITHOUT EXPRESS WRITTEN PERMISSION. NO PERMISSION TO MODIFY OR REPRODUCE ANY OF THESE ARCHITECTURAL WORKS, INCLUDING WITHOUT LIMITATION THE CONSTRUCTION OF ANY BUILDING, IS EXPRESSED, OR SHOULD BE IMPLIED FROM DELIVERY OF PRELIMINARY DRAWINGS OR UNSEALED CONSTRUCTION DOCUMENTS. PERMISSION TO CONSTRUCT THE BUILDING DEPICTED IN SEALED CONSTRUCTION DRAWINGS IS EXPRESSLY CONDITIONED ON THE FULL AND TIMELY PAYMENT OF ALL THE FEES OTHERWISE DUE RESIDENTIAL DESIGNED SOLUTIONS, INC. AND IN THE ABSENCE OF ANY WRITTEN AGREEMENT TO THE CONTRARY, IS LIMITED TO A ONE-TIME USE ON THE SITE INDICATED ON THESE PLANS. ANY OTHER REPRODUCTION, REUSE, OR MODIFICATION OF THESE PLANS OR THE ARCHITECTURAL WORK DEPICTED IS PROHIBITED.

DSN	DL	04.20.2023
LAY	JM	06.09.2023
DET	JM	08.16.2023
CHK	DL	08.17.2023
ENGR	JM	08.21.2023

SHEET:
A.3